Voitures :
- Ne doit pas être inférieur à une place de stationnement par tranche de 70 m² de surface de plancher pour les constructions à destination d'habitation ;
- Un minimum de 20% du quota de stationnement doit être réalisé en surface afin d'assurer le stationnement nécessaire au fonctionnement du site ;
- 50% des places de stationnement réalisées doivent être intégrées dans le volume d'une construction.

Vélo :
Ne doit pas être inférieure à 1,5 m² par tranche de 70 m² de surface de plancher pour les constructions à destination d'habitation.

Calculs :
SDP = 999,1 m² / 70 = 14,2
soit 14 places de stationnements
dont 3 en extérieurs

Local vélo : 999,1 / 70 X 1,5 = 21,4 m²

Le projet prévoit :
- 8 boxs de 2 places voitures et 2 places deux-roues chacun
- 4 places extérieures de stationnement dont 1 PMR
- Un local vélo clos et couvert facilement accessible depuis la voie publique de 22,2 m²

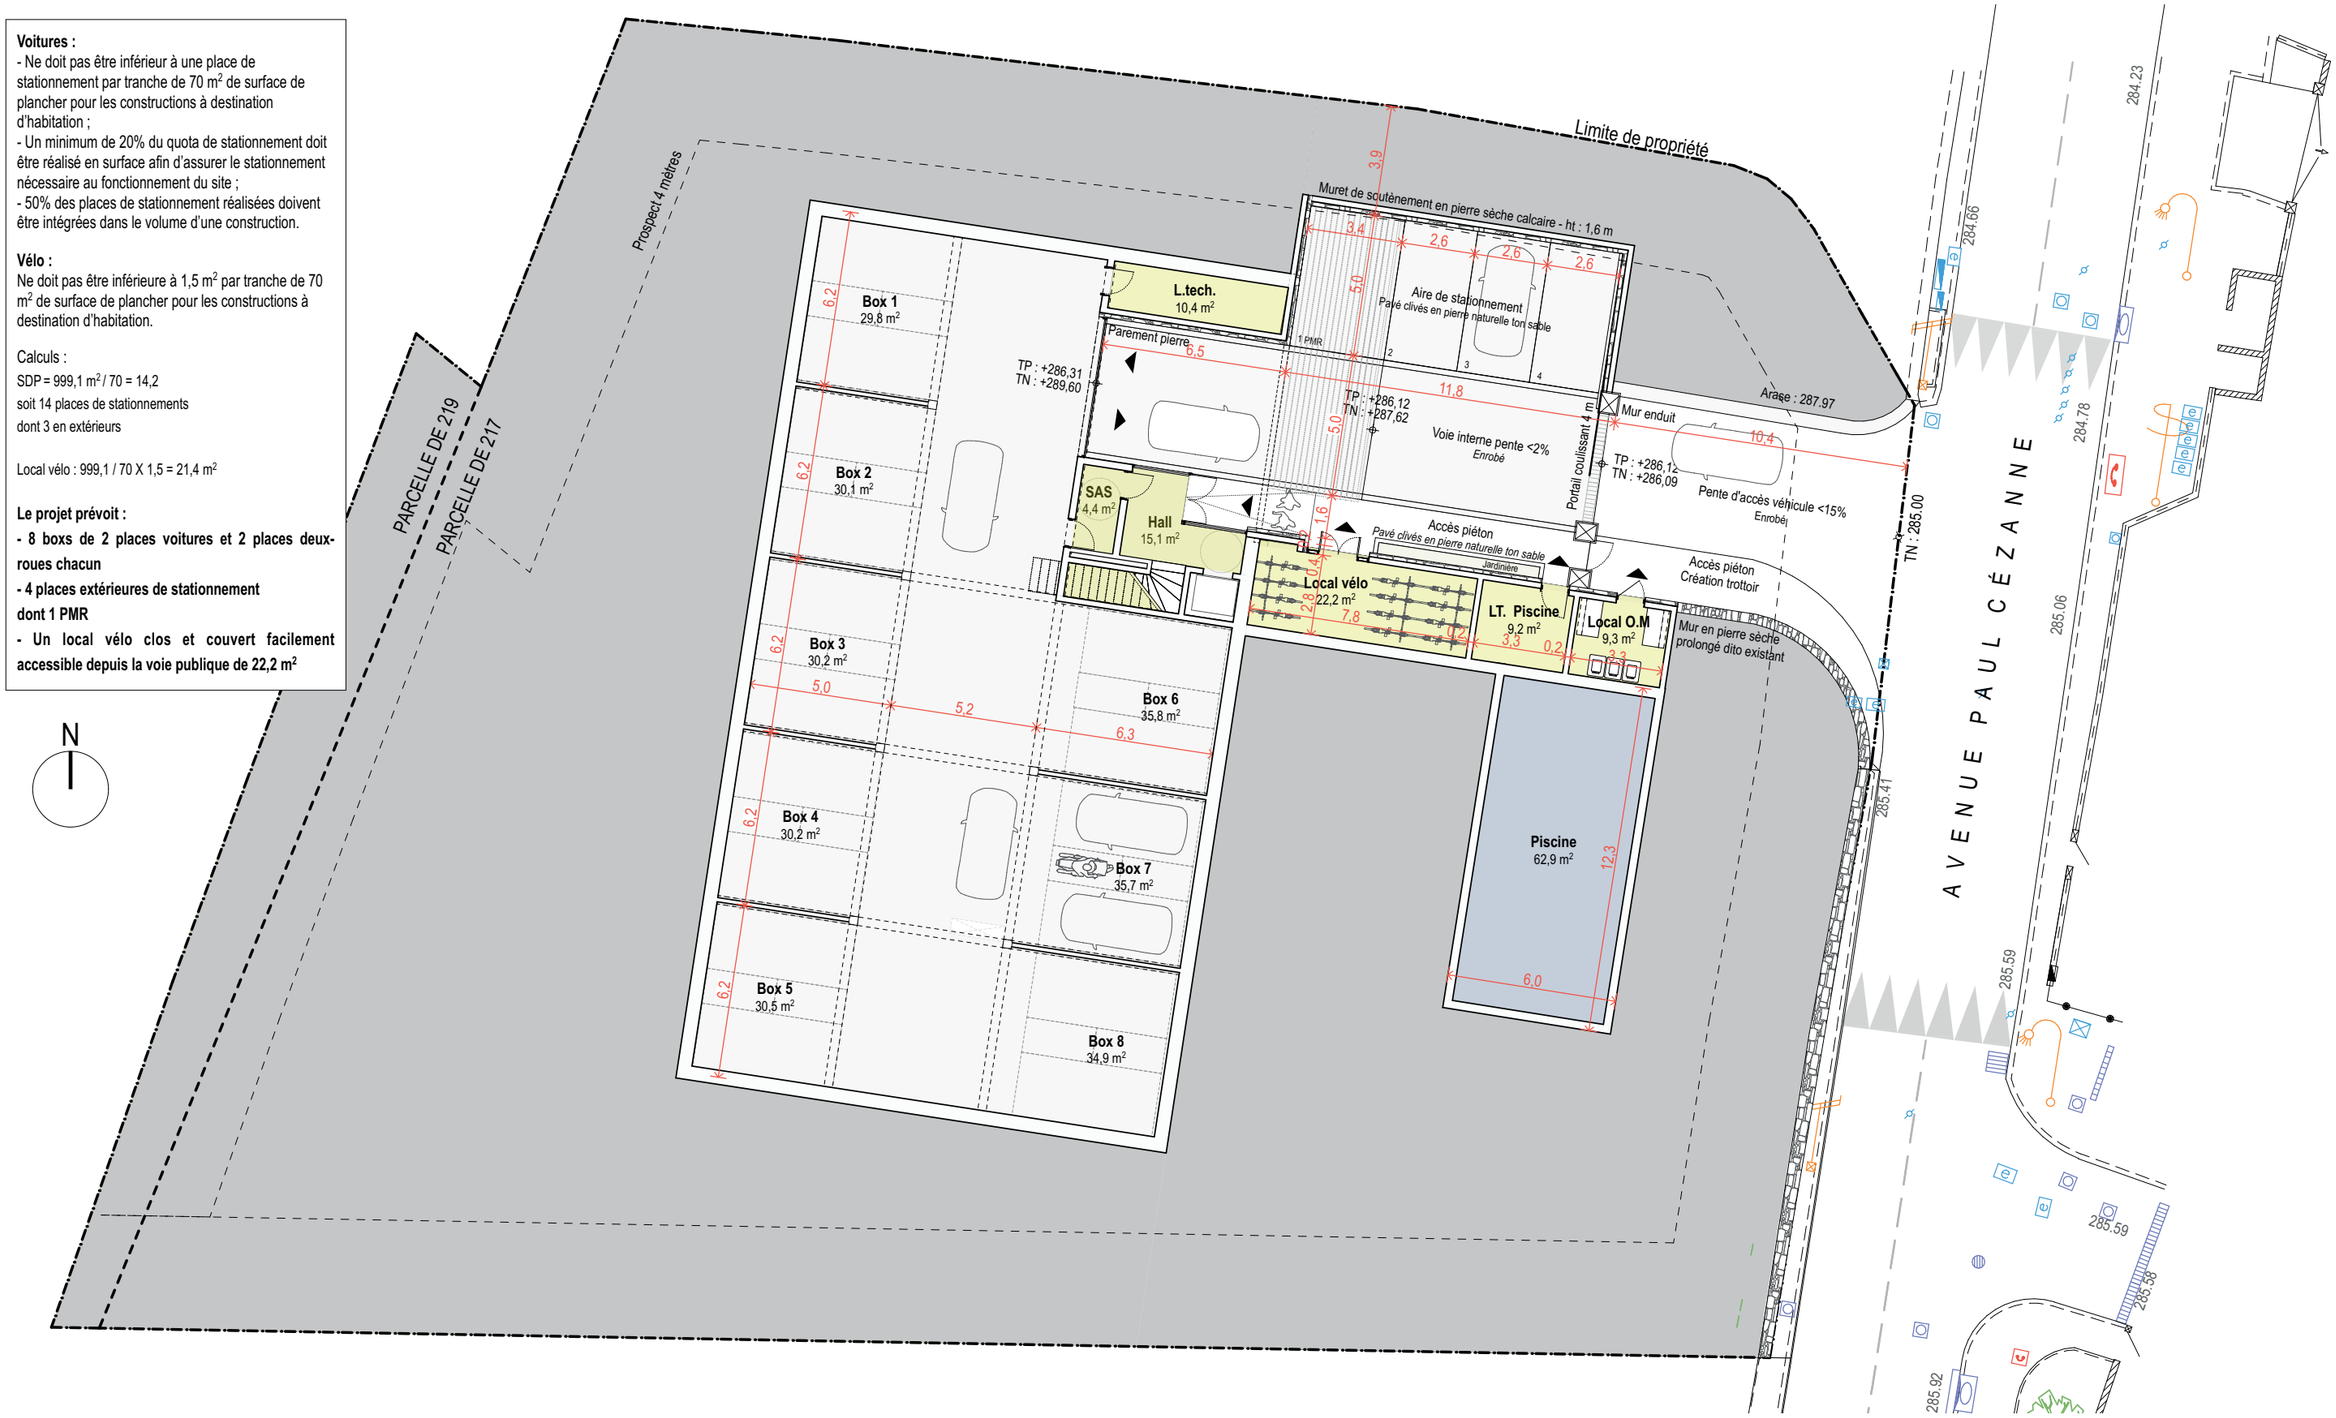

STATIONNEMENT & LOCAUX ANNEXES

CONSTRUCTION D'UN IMMEUBLE COLLECTIF EN R+1 DE 8 LOGEMENTS // 59 AVENUE PAUL CÉZANNE - AIX-EN-PROVENCE